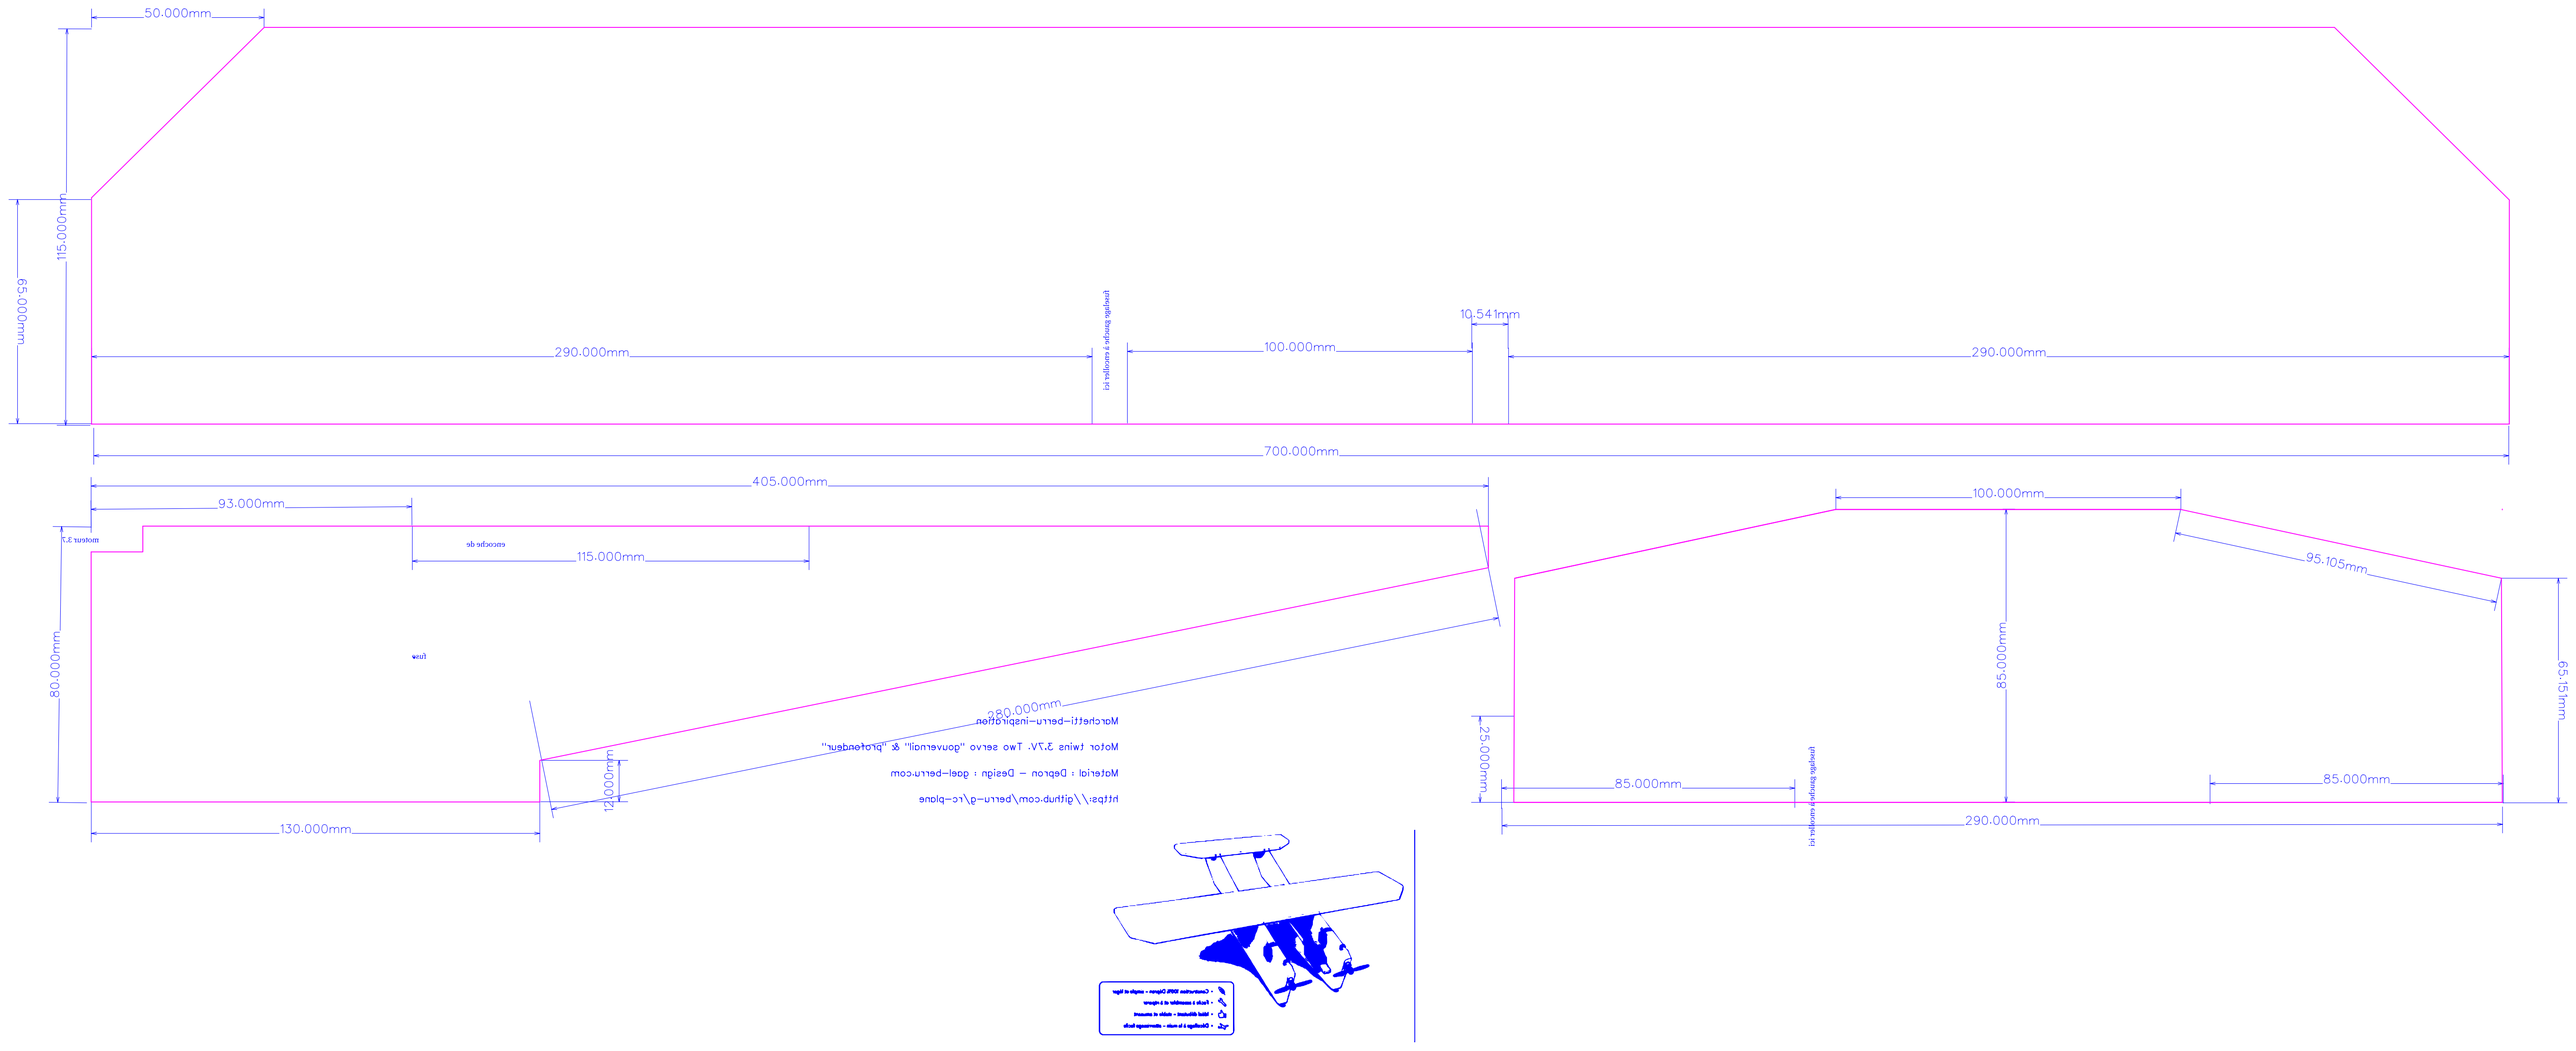
50.000mm
115.000mm
65.000mm
290.000mm
100.000mm
10.541mm
290.000mm
700.000mm
405.000mm
93.000mm
115.000mm
80.000mm
280.000mm
12.000mm
130.000mm
100.000mm
95.105mm
85.000mm
65.151mm
25.000mm
85.000mm
85.000mm
290.000mm